


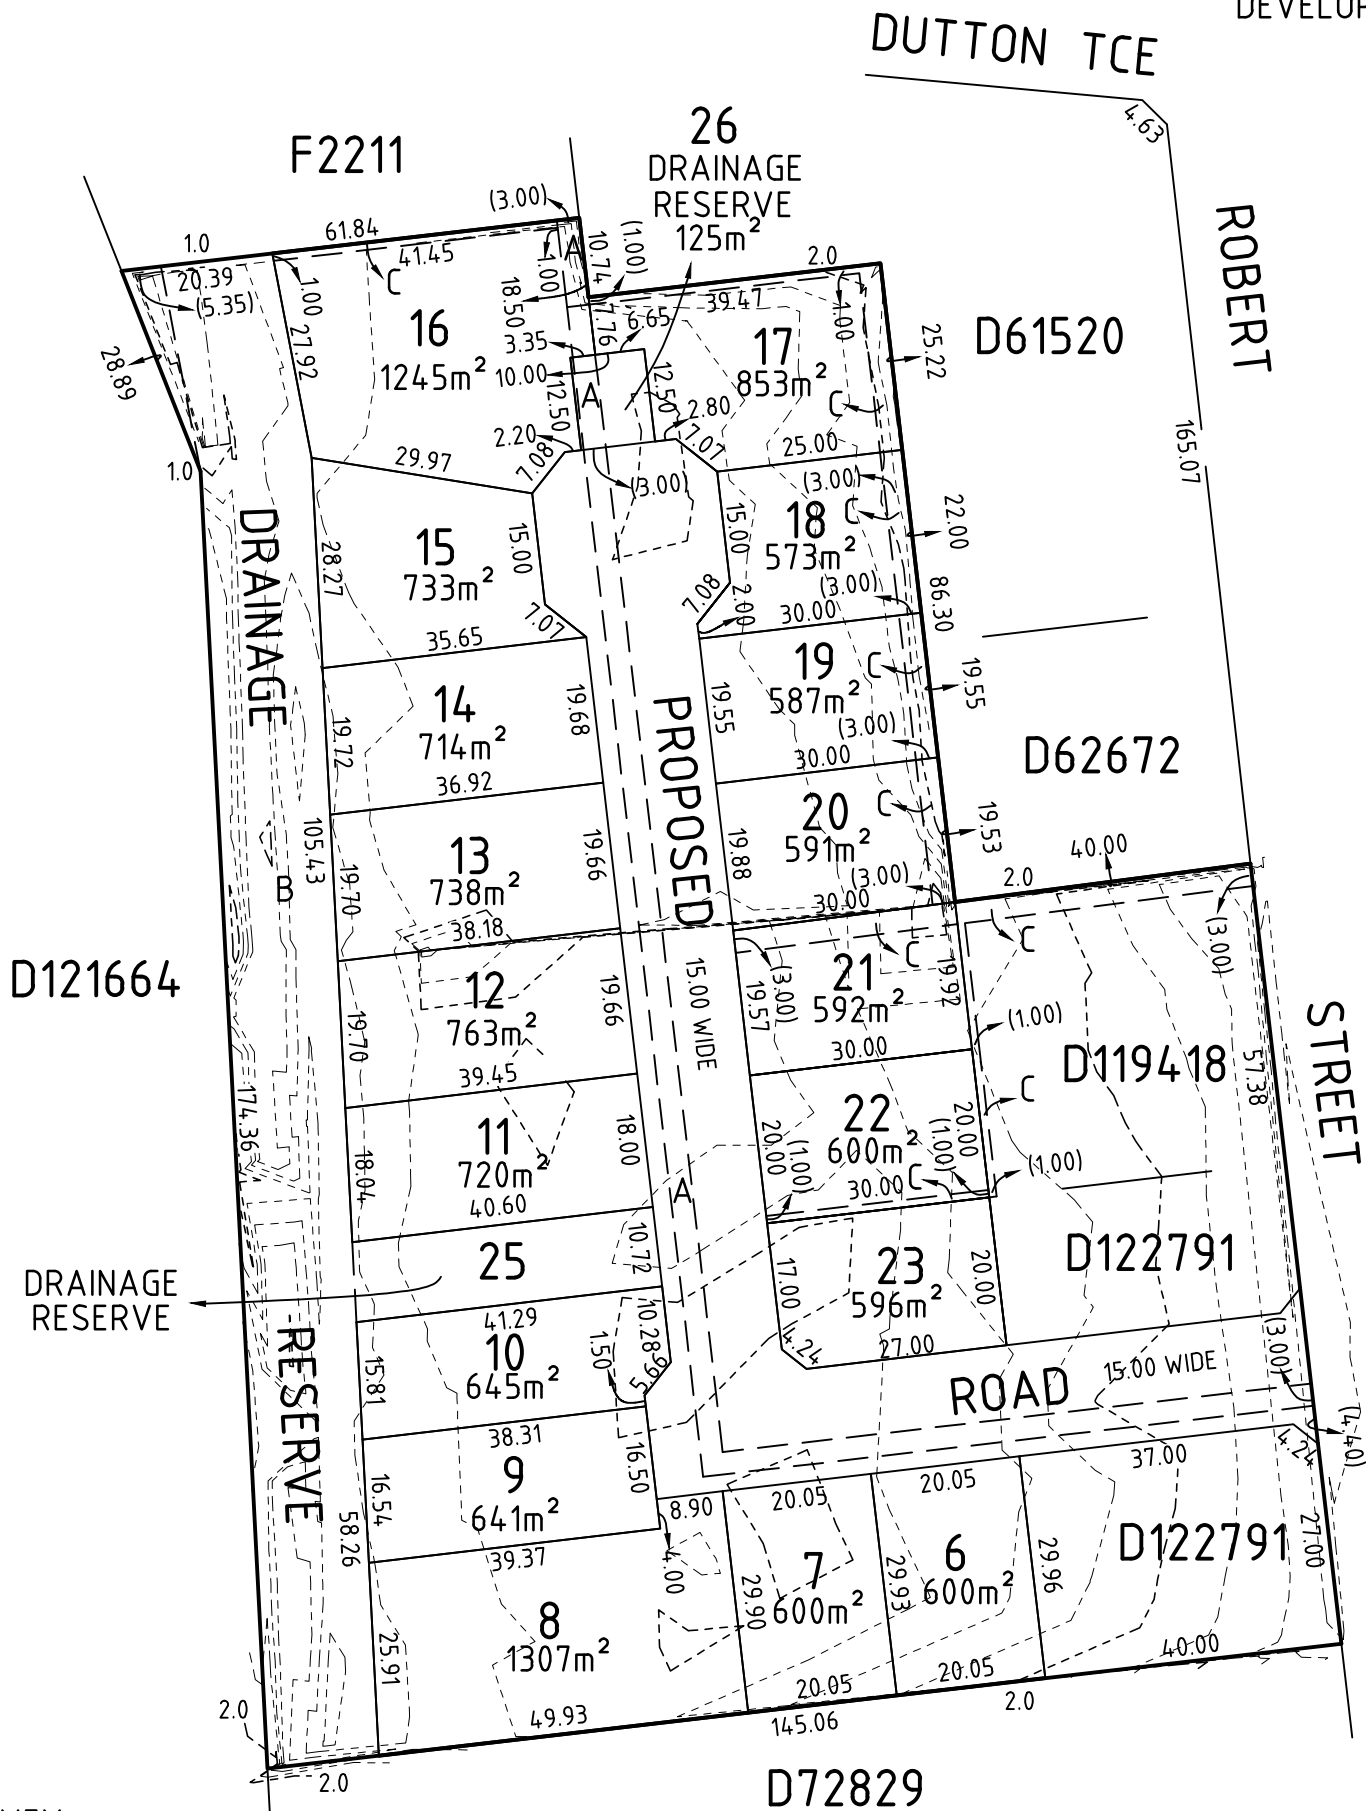


SUBJECT TO SURVEY
APPROVAL

PORTION OF ALLOTMENT 16, 26 (DRAINAGE RESERVE)
AND PROPOSED ROAD MARKED A IS SUBJECT TO AN
EASEMENT TO THE COUNCIL FOR THE AREA
(AQ 6544444)

PORTION OF ALLOTMENTS 16-22 INCL MARKED C IS
TO BE SUBJECT TO AN EASEMENT TO THE COUNCIL
FOR THE AREA FOR DRAINAGE PURPOSES

Vouched for in accordance with
Schedule 5 of Development Act 1993

Signature
3/8/15
Licensed Surveyor

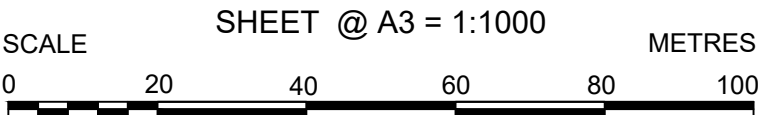

 HENNIG & CO PTY LTD LICENSED SURVEYORS <i>Sub Division Experts!</i> 275 Marion Road, North Plympton S.A. 5037 Ph: (08)82970883 Fax: (08)82971170 Email: hennig @ hennig.com.au	Parcel Information		Survey Information		Job Number 16536		Survey Type	
	HUNDRED OF: HUTCHINSON		BEARING DATUM: MGA		Date of Plan 29-06-2022		IDENTIFICATION ☐	
	ALLOTMENT 72 IN D60440		ELEVATION DATUM: AHD				DETAIL ☐	
	AREA OF: TUMBY BAY		ORIGIN OF LEVELS:		SET OUT ☐			
	CT 6081/443		PSM 6129/1006		DAP ☒			
			CONTOUR INTERVAL: 0.25m		Surveyor SBH		Draftsperson JMV	
							Revision Rev A	