

Site Coverage (Unison Modular)	
Site Area	19,981m ²
Proposed Site Coverage	20%

House Type	House Area	Deck Area	Quantity	Total House Area
Type 1A	104m ²	24m ²	15	1,560m ²
Type 1B	104m ²	24m ²	4	416m ²
Type 2A	114m ²	24m ²	12	1,368m ²
Type 2B	114m ²	24m ²	4	456m ²
Type 2C	114m ²	24m ²	2	228m ²
Total Unit Area				4,028m ²

Site Coverage (As Per Glenorchy Interim Planning Scheme 2015)	
Site Area	19,981m ²
Proposed Site Coverage	18%

House Type	House Area	Deck Area	Quantity	Total House Area
Type A	93m ²	24m ²	4	372m ²
Type B	93m ²	24m ²	1	93m ²
Type C	106m ²	24m ²	2	212m ²
Type D	93m ²	24m ²	15	1,395m ²
Type E	112m ²	24m ²	5	560m ²
Type F	112m ²	24m ²	1	112m ²
Type G	108m ²	24m ²	6	648m ²
Type H	93m ²	24m ²	1	93m ²
Type I	93m ²	24m ²	2	186m ²
Total Unit Area				3,671m ²

KEY

EASEMENT - REFER TO CIVIL DOCUMENTATION FOR DETAILS

RIGHT OF WAY - REFER TO CIVIL DOCUMENTATION FOR DETAILS

PROPOSED DRIVEWAY, PARKING & HARDSTAND. REFER TO CIVIL DOCUMENTATION FOR DETAILS.

PROPOSED CONCRETE PATH.

MIN. 24m² PRIVATE OPEN SPACE (DECK) - 4.0m x 6.0m AS PER GLENORCHY INTERIM PLANNING SCHEME 2015 CLAUSE 10.4.3 - A2

MIN. 24m² PRIVATE OPEN SPACE (LANDSCAPE) - 4.0m x 6.0m AS PER GLENORCHY INTERIM PLANNING SCHEME 2015 CLAUSE 10.4.3 - A2

COMMON AREA LANDSCAPING


EXISTING PROPOSAL (PLANNING APPROVAL)

PROPOSED NEW DECK (UNISON MODULAR)

BOUNDARY SETBACK AS PER GLENORCHY INTERIM PLANNING SCHEME 2015

PROPOSED NEW BUILDING LINE (UNISON MODULAR)

Site Plan

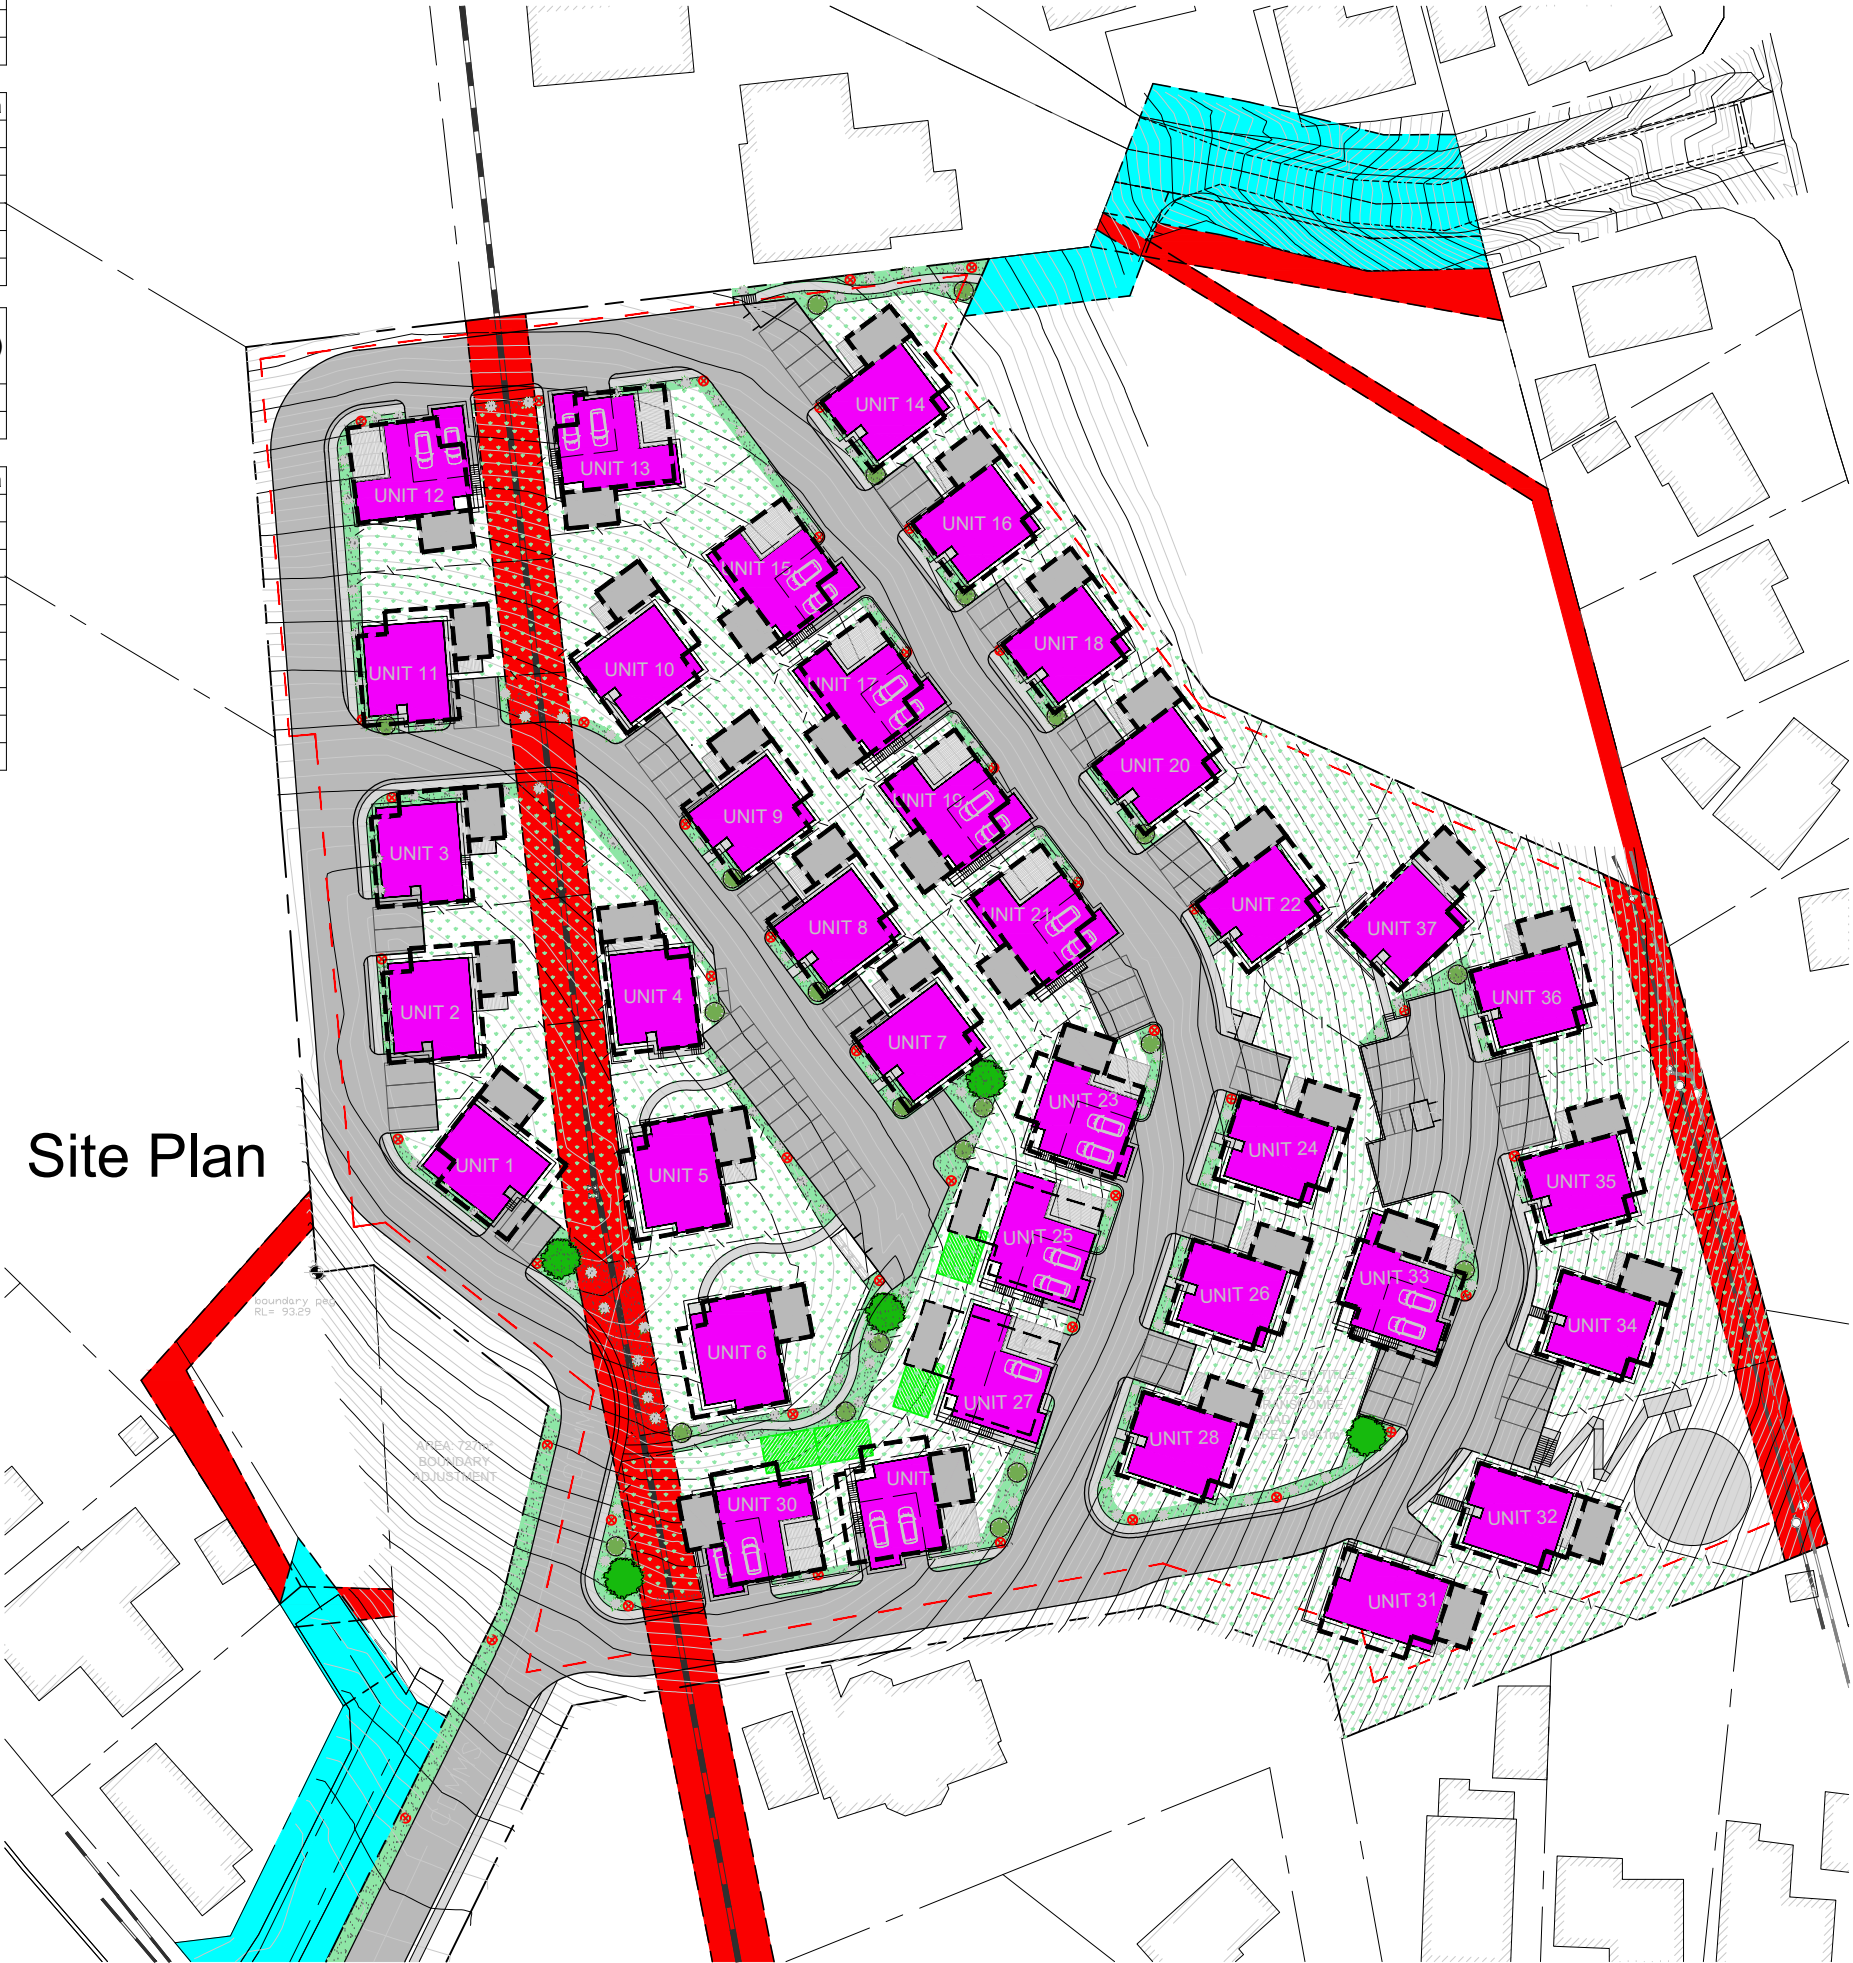

PROJECT NAME:
Branscombe Road

CLIENT:
Factory2Key

SPONSOR:

INSTALLATION LOCATION:

BUILDING AUTHORITY AND COMPLIANCE:

MANUFACTURER:

MANUFACTURER LOCATION:

PREPARED AND ISSUED BY:
Division of Unison Project Malaysia Sdn Bhd
201801042793 (1304825-A)
33, Jalan SS18/6, 47500 Subang Jaya,
Selangor Darul Ehsan, Malaysia
www.unisonmodular.com

REVISION			
No.	Description	Date	By
A	Preliminary Drawing	06Mar26	Rzl
B	Preliminary Drawing	09Mar26	Rzl

SIGNED BY CLIENT/SPONSOR:

SIGNED FOR ISSUE BY UNISON MODULAR:

RELEASE STATUS:

Preliminary Drawing

PROJECT NO:
25606

RELEASE DATE:

BUILDING NAME:

DRAWING TITLE:
SITE PLAN

APPR'VED BY:
MW

DRAWN BY:
RZL

CHECK BY:
MW

SCALE:
1 : 800

DATE:
09Mar26

DRAWING NO:
A100

REV:
B